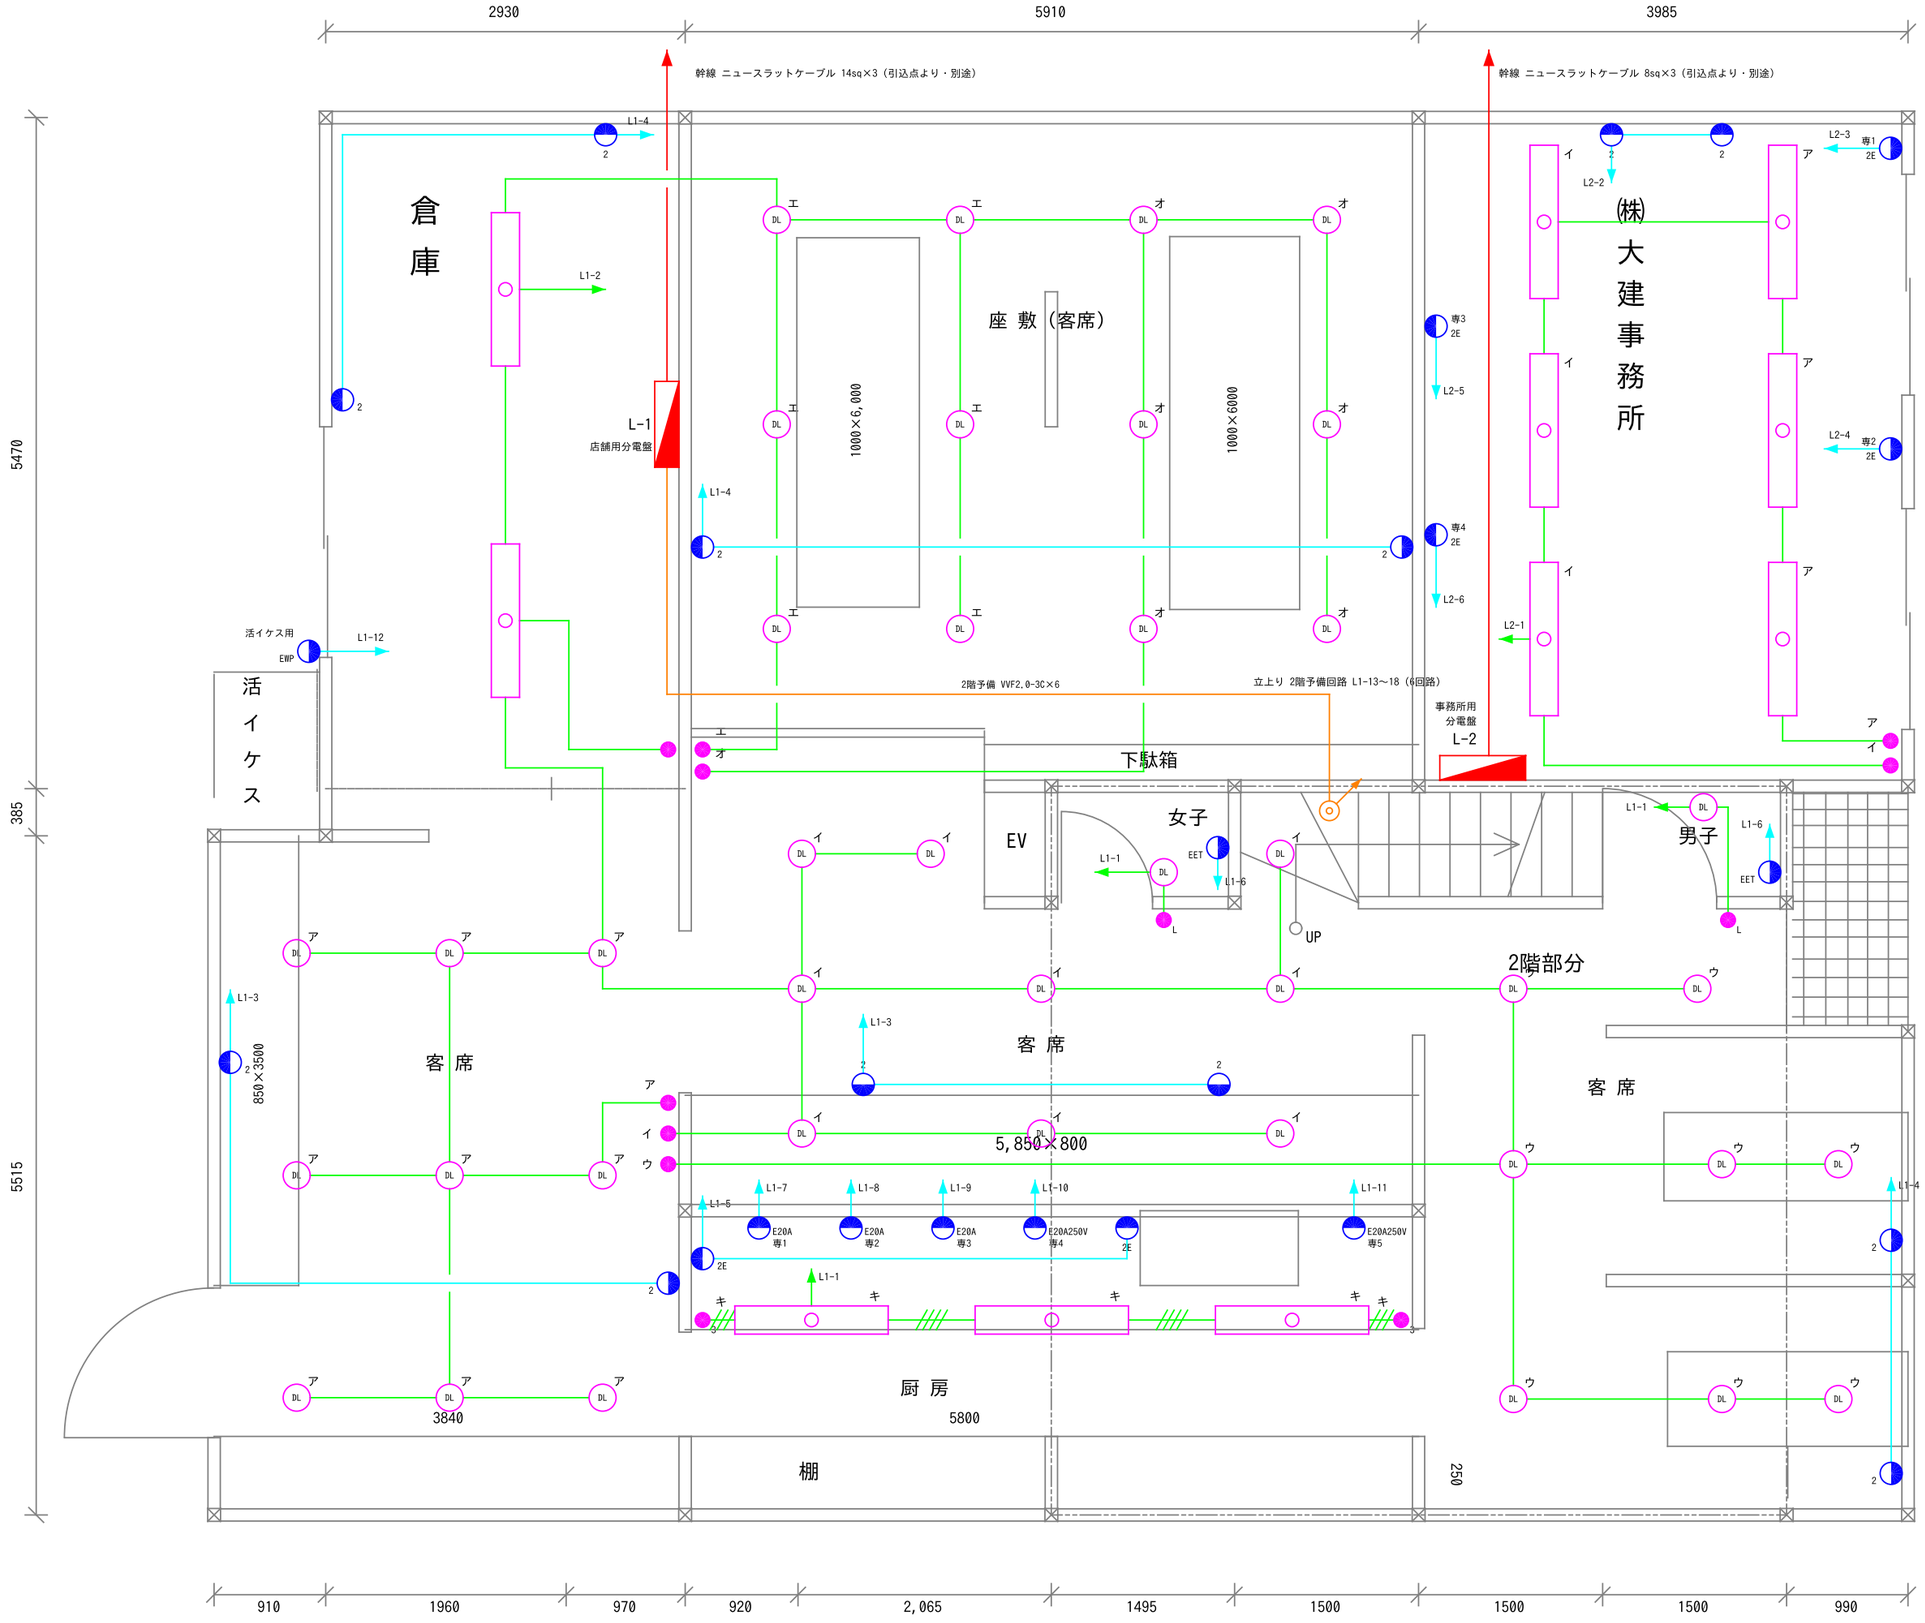


N

凡　例

- LEDダウンライト φ100 埋込 — 1,000lm 電球色 約8.5W
- LEDベースライト 40形 逆富士 — 直付 6,900lm 昼白色 約45W
- 片切スイッチ 15A — FL+1,300
- 3路スイッチ 15A — FL+1,300
- 確認表示灯内蔵スイッチ — FL+1,300（便所）
- 2口コンセント 15A125V — FL+300
- 2口コンセント 接地極付 — FL+300
- コンセント 接地極付接地端子付 — FL+300（温水洗浄便座用）
- 専用コンセント 接地極付 20A125V — FL+300（厨房 機器未定）
- 専用コンセント 接地極付 20A250V — FL+300（厨房 機器未定）
- 防雨形コンセント 接地極付 — FL+300（屋外 活イケス用）
- 分電盤 — L-1 店舗用 / L-2 事務所用
- 天井隠ぺい配線 — 電灯 VVF1.6-2C / コンセント VVF2.0-2C
- 同上 3本（数字＝電線本数） — VVF1.6-3C　4本は VVF1.6-2C×2
- 分電盤へ（ホームラン） — 傍記＝盤名-回路番号
- 立上り（2階へ）
- 配線交差部 — 縦方向（Y方向）の配線を切断して表示
- ア 点滅区分記号 — 同記号のスイッチで点滅

【特記】

1. 天井高 CH=2,400
2. 取付高さ（特記なき限り）
   スイッチ FL+1,300 / コンセント FL+300
3. 照度計算（光束法）
   客席・座敷・便所 DL 床面200lx
   倉庫200lx(床面) 厨房500lx・
   事務所750lx(作業面FL+850)
4. 厨房専用回路(専1～5)は機器未定の
   ため仮設定。機器確定後に電圧・
   容量・形状・取付高さを確認
5. 2階予備6回路は L-1 に確保し、
   階段部で立上り(行先は2階計画後)
6. 引込点・電力量計・弱電・空調・
   換気扇・EV電源は別途

図名	電灯・コンセント設備平面図
縮尺	1/50 (A3)
単位	mm
原図	平面図 heimenzu02 より作図
作成	2026-10-04