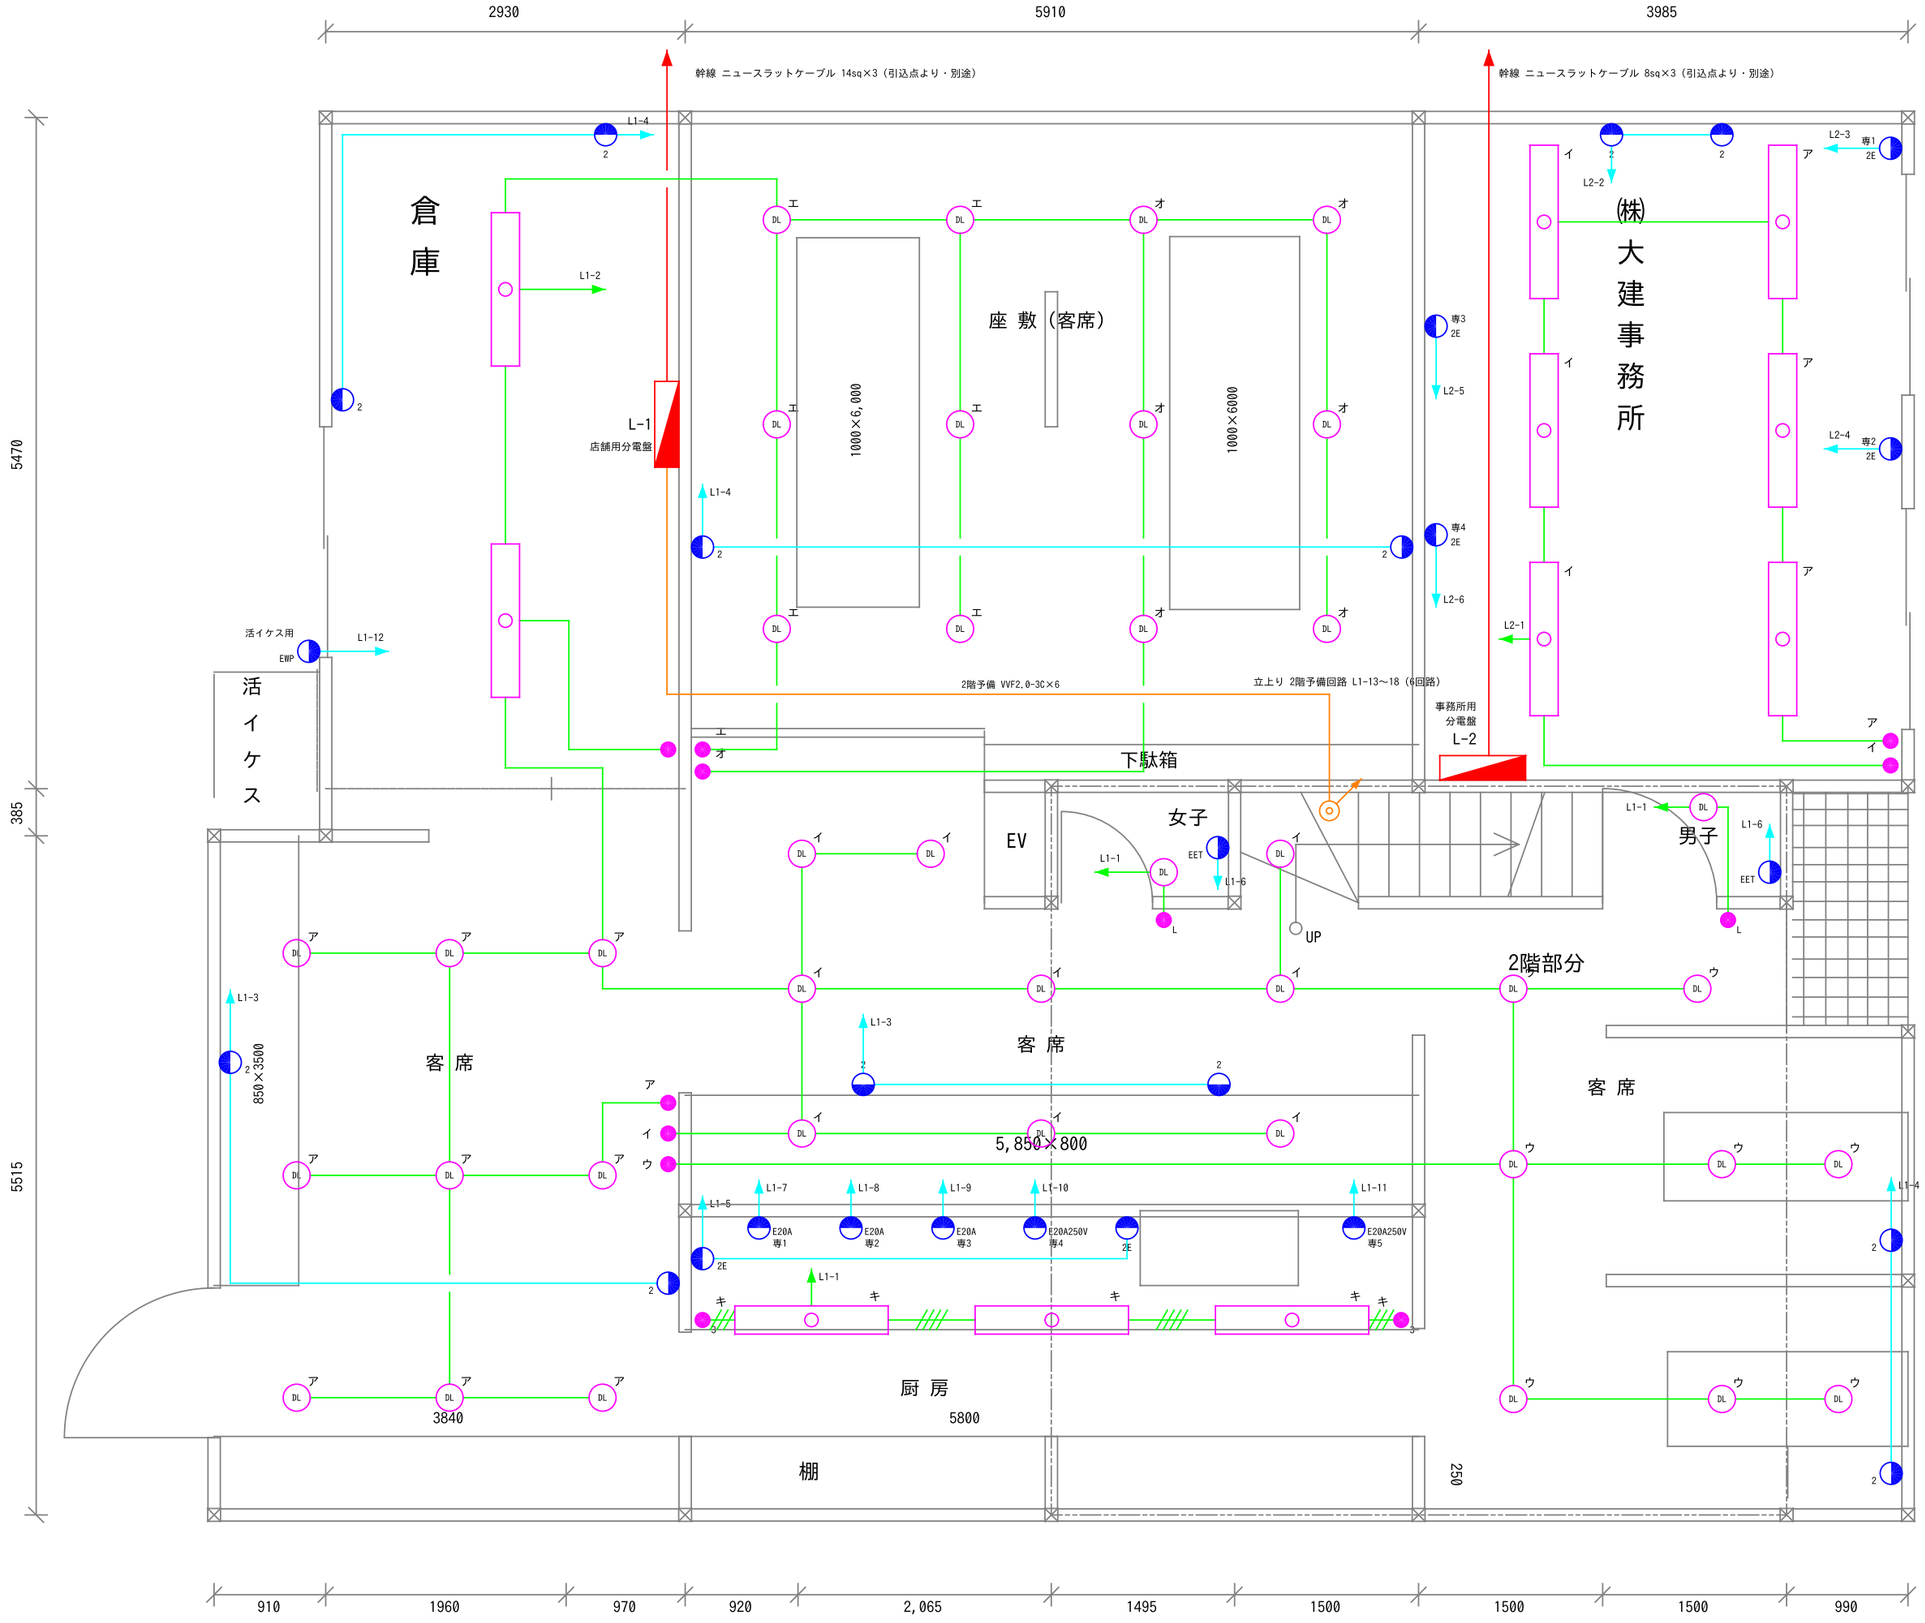


N

凡　例

- LEDダウンライト φ100 埋込 — 1,000lm 電球色 約8.5W
- LEDベースライト 40形 逆富士 — 直付 6,900lm 昼白色 約45W
- 片切スイッチ 15A — FL+1,300
- 3路スイッチ 15A — FL+1,300
- 確認表示灯内蔵スイッチ — FL+1,300（便所）
- 2口コンセント 15A125V — FL+300
- 2口コンセント 接地極付 — FL+300
- コンセント 接地極付接地端子付 — FL+300（温水洗浄便座用）
- 専用コンセント 接地極付 20A125V — FL+300（厨房 機器未定）
- 専用コンセント 接地極付 20A250V — FL+300（厨房 機器未定）
- 防雨形コンセント 接地極付 — FL+300（屋外 活イケス用）
- 分電盤 — L-1 店舗用 / L-2 事務所用
- 天井隠ぺい配線 — 電灯 VVF1.6-2C / コンセント VVF2.0-2C
- 同上 3本（数字＝電線本数） — VVF1.6-3C　4本は VVF1.6-2C×2
- 分電盤へ（ホームラン） — 傍記＝盤名-回路番号
- 立上り（2階へ）
- 配線交差部 — 縦方向（Y方向）の配線を切断して表示
- ア 点滅区分記号 — 同記号のスイッチで点滅

【特記】

1. 天井高 CH=2,400
2. 取付高さ（特記なき限り）
   スイッチ FL+1,300 / コンセント FL+300
3. 照度計算（光束法）
   客席・座敷・便所 DL 床面200lx
   倉庫200lx(床面) 厨房500lx・
   事務所750lx(作業面FL+850)
4. 厨房専用回路(専1～5)は機器未定の
   ため仮設定。機器確定後に電圧・
   容量・形状・取付高さを確認
5. 2階予備6回路は L-1 に確保し、
   階段部で立上り(行先は2階計画後)
6. 引込点・電力量計・弱電・空調・
   換気扇・EV電源は別途

図名	電灯・コンセント設備平面図
縮尺	1/50 (A3)
単位	mm
原図	平面図 heimenzu02 より作図
作成	2026-10-04

店舗用分電盤 L-1　結線図

設置場所：倉庫　電気方式：1φ3W 100/200V　幹線：ニュースラットケーブル 14sq×3

幹線 ニュースラットケーブル 14sq×3（引込点より）

B　主幹 MCCB 3P 60AF/60AT

	回路	遮断器	電線	負荷名称	容量VA	相	備考
E	L1-1	ELB 2P2E 20AF/20AT 30mA	VVF1.6-2C/3C	電灯（水回り：厨房・便所）	152	R	
B	L1-2	MCB 2P1E 20AF/20AT	VVF1.6-2C	電灯（客席・座敷・倉庫）	413	T	
B	L1-3	MCB 2P1E 20AF/20AT	VVF2.0-2C	コンセント（客席 入口・カウンター）	600	R	
B	L1-4	MCB 2P1E 20AF/20AT	VVF2.0-2C	コンセント（倉庫・座敷・ボックス席）	900	T	
E	L1-5	ELB 2P2E 20AF/20AT 30mA	VVF2.0-3C	コンセント（厨房 一般）	300	R	
E	L1-6	ELB 2P2E 20AF/20AT 30mA	VVF2.0-3C	コンセント（便所 温水洗浄便座）	1,400	T	想定 700VA×2
E	L1-7	ELB 2P2E 20AF/20AT 30mA	VVF2.0-3C	厨房専用1 100V	1,500	R	機器未定・想定
E	L1-8	ELB 2P2E 20AF/20AT 30mA	VVF2.0-3C	厨房専用2 100V	1,500	T	機器未定・想定
E	L1-9	ELB 2P2E 20AF/20AT 30mA	VVF2.0-3C	厨房専用3 100V	1,500	R	機器未定・想定
E	L1-10	ELB 2P2E 20AF/20AT 30mA	VVF2.0-3C	厨房専用4 200V	2,000	RT	機器未定・想定
E	L1-11	ELB 2P2E 20AF/20AT 30mA	VVF2.0-3C	厨房専用5 200V	2,000	RT	機器未定・想定
E	L1-12	ELB 2P2E 20AF/20AT 30mA	VVF2.0-3C	活イケス専用（屋外 防雨）	1,000	T	想定
B	L1-13	MCB 2P2E 20AF/20AT	VVF2.0-3C	2階予備1	–	–	2階計画後に確定
B	L1-14	MCB 2P2E 20AF/20AT	VVF2.0-3C	2階予備2	–	–	2階計画後に確定
B	L1-15	MCB 2P2E 20AF/20AT	VVF2.0-3C	2階予備3	–	–	2階計画後に確定
B	L1-16	MCB 2P2E 20AF/20AT	VVF2.0-3C	2階予備4	–	–	2階計画後に確定
B	L1-17	MCB 2P2E 20AF/20AT	VVF2.0-3C	2階予備5	–	–	2階計画後に確定
B	L1-18	MCB 2P2E 20AF/20AT	VVF2.0-3C	2階予備6	–	–	2階計画後に確定
B	L1-19	MCB 2P1E 20AF/20AT	–	予備	–	–	スペース
B	L1-20	MCB 2P1E 20AF/20AT	–	予備	–	–	スペース

設備容量 合計 13,265 VA（R相 6,052 VA / T相 7,213 VA）

需要率 0.8 として 最大相電流 ≒ 7,213×0.8÷100V ≒ 58 A　→ 主幹 60AF/60AT にて可

幹線・共通事項

・幹線　店舗 L-1：ニュースラットケーブル 14sq×3（1φ3W 100/200V）

　　事務所 L-2：ニュースラットケーブル 8sq×3（1φ3W 100/200V）

・引込点・電力量計は別途。幹線の亘長確定後に電圧降下を確認すること

・2階予備 L1-13〜18 は容量未計上。2階負荷確定時に主幹・幹線容量を再検討

・水回り（厨房・便所）・屋外・厨房専用回路は漏電遮断器(30mA)とする

・コンセント接地(E)は分電盤の接地端子より（D種接地）

事務所用分電盤 L-2　結線図

設置場所：事務所　電気方式：1φ3W 100/200V　幹線：ニュースラットケーブル 8sq×3

幹線 ニュースラットケーブル 8sq×3（引込点より）

B　主幹 MCCB 3P 50AF/40AT

	回路	遮断器	電線	負荷名称	容量VA	相	備考
B	L2-1	MCB 2P1E 20AF/20AT	VVF1.6-2C	電灯（事務所）	270	R	
B	L2-2	MCB 2P1E 20AF/20AT	VVF2.0-2C	コンセント（事務所 一般）	300	T	
B	L2-3	MCB 2P1E 20AF/20AT	VVF2.0-3C	OA専用1	1,200	R	想定
B	L2-4	MCB 2P1E 20AF/20AT	VVF2.0-3C	OA専用2	1,200	T	想定
B	L2-5	MCB 2P1E 20AF/20AT	VVF2.0-3C	OA専用3	1,200	R	想定
B	L2-6	MCB 2P1E 20AF/20AT	VVF2.0-3C	OA専用4	1,200	T	想定
B	L2-7	MCB 2P1E 20AF/20AT	–	予備	–	–	スペース
B	L2-8	MCB 2P1E 20AF/20AT	–	予備	–	–	スペース

設備容量 合計 5,370 VA（R相 2,670 VA / T相 2,700 VA）

需要率 0.8 として 最大相電流 ≒ 2,700×0.8÷100V ≒ 22 A　→ 主幹 50AF/40AT にて可

照度計算表（光束法　N = E・A ／（F・U・M））

室名	面積㎡	基準面	室指数	器具	光束lm	照明率	保守率	設計照度	必要台数	設置台数	計算照度
座敷（客席）	28.98	床面	1.12	ダウンライト	1,000	0.68	0.77	200lx	11.0	12台	218lx
客席（入口・レジ付近）	20.33	床面	0.92	ダウンライト	1,000	0.64	0.77	200lx	8.3	9台	217lx
客席（カウンター・通路）	18.42	床面	0.71	ダウンライト	1,000	0.57	0.77	200lx	8.4	9台	214lx
客席（ボックス席）	18.18	床面	0.90	ダウンライト	1,000	0.63	0.77	200lx	7.5	8台	214lx
便所（女子）	1.18	床面	0.22	ダウンライト	1,000	0.38	0.77	200lx	0.8	1台	250lx
便所（男子）	1.19	床面	0.22	ダウンライト	1,000	0.38	0.77	200lx	0.8	1台	249lx
厨房	13.99	作業面 FL+850	1.09	ベースライト	6,900	0.60	0.69	500lx	2.5	3台	611lx
倉庫	15.28	床面	0.77	ベースライト	6,900	0.51	0.77	200lx	1.1	2台	355lx
事務所	20.81	作業面 FL+850	1.45	ベースライト	6,900	0.66	0.77	750lx	4.4	6台	1015lx

・天井高 2,400。床面基準は H=2.4m、作業面(FL+850)基準は H=1.55m で室指数を算出

・照明率は反射率 天井70%・壁50%・床10% の一般的な値（器具選定後にメーカー照明率表で再確認）

・保守率 0.77（LED・普通環境）、厨房は 0.69（汚れやすい環境）

・ダウンライト：φ100 埋込 1,000lm（約8.5W）　ベースライト：40形 逆富士 6,900lm（約45W）

・設計照度は JIS Z 9110 を参考（飲食店客席・便所 200lx 以上、調理室 500lx、事務室 750lx）

・事務所は 2列×3灯（窓側ア／内側イ）の配置で計算照度 約1,000lx（750lx 以上を確保）

図名	分電盤結線図・照度計算表
縮尺	NonScale（A3）
単位	mm / VA
原図	電灯・コンセント設備平面図による
作成	2026-10-04